


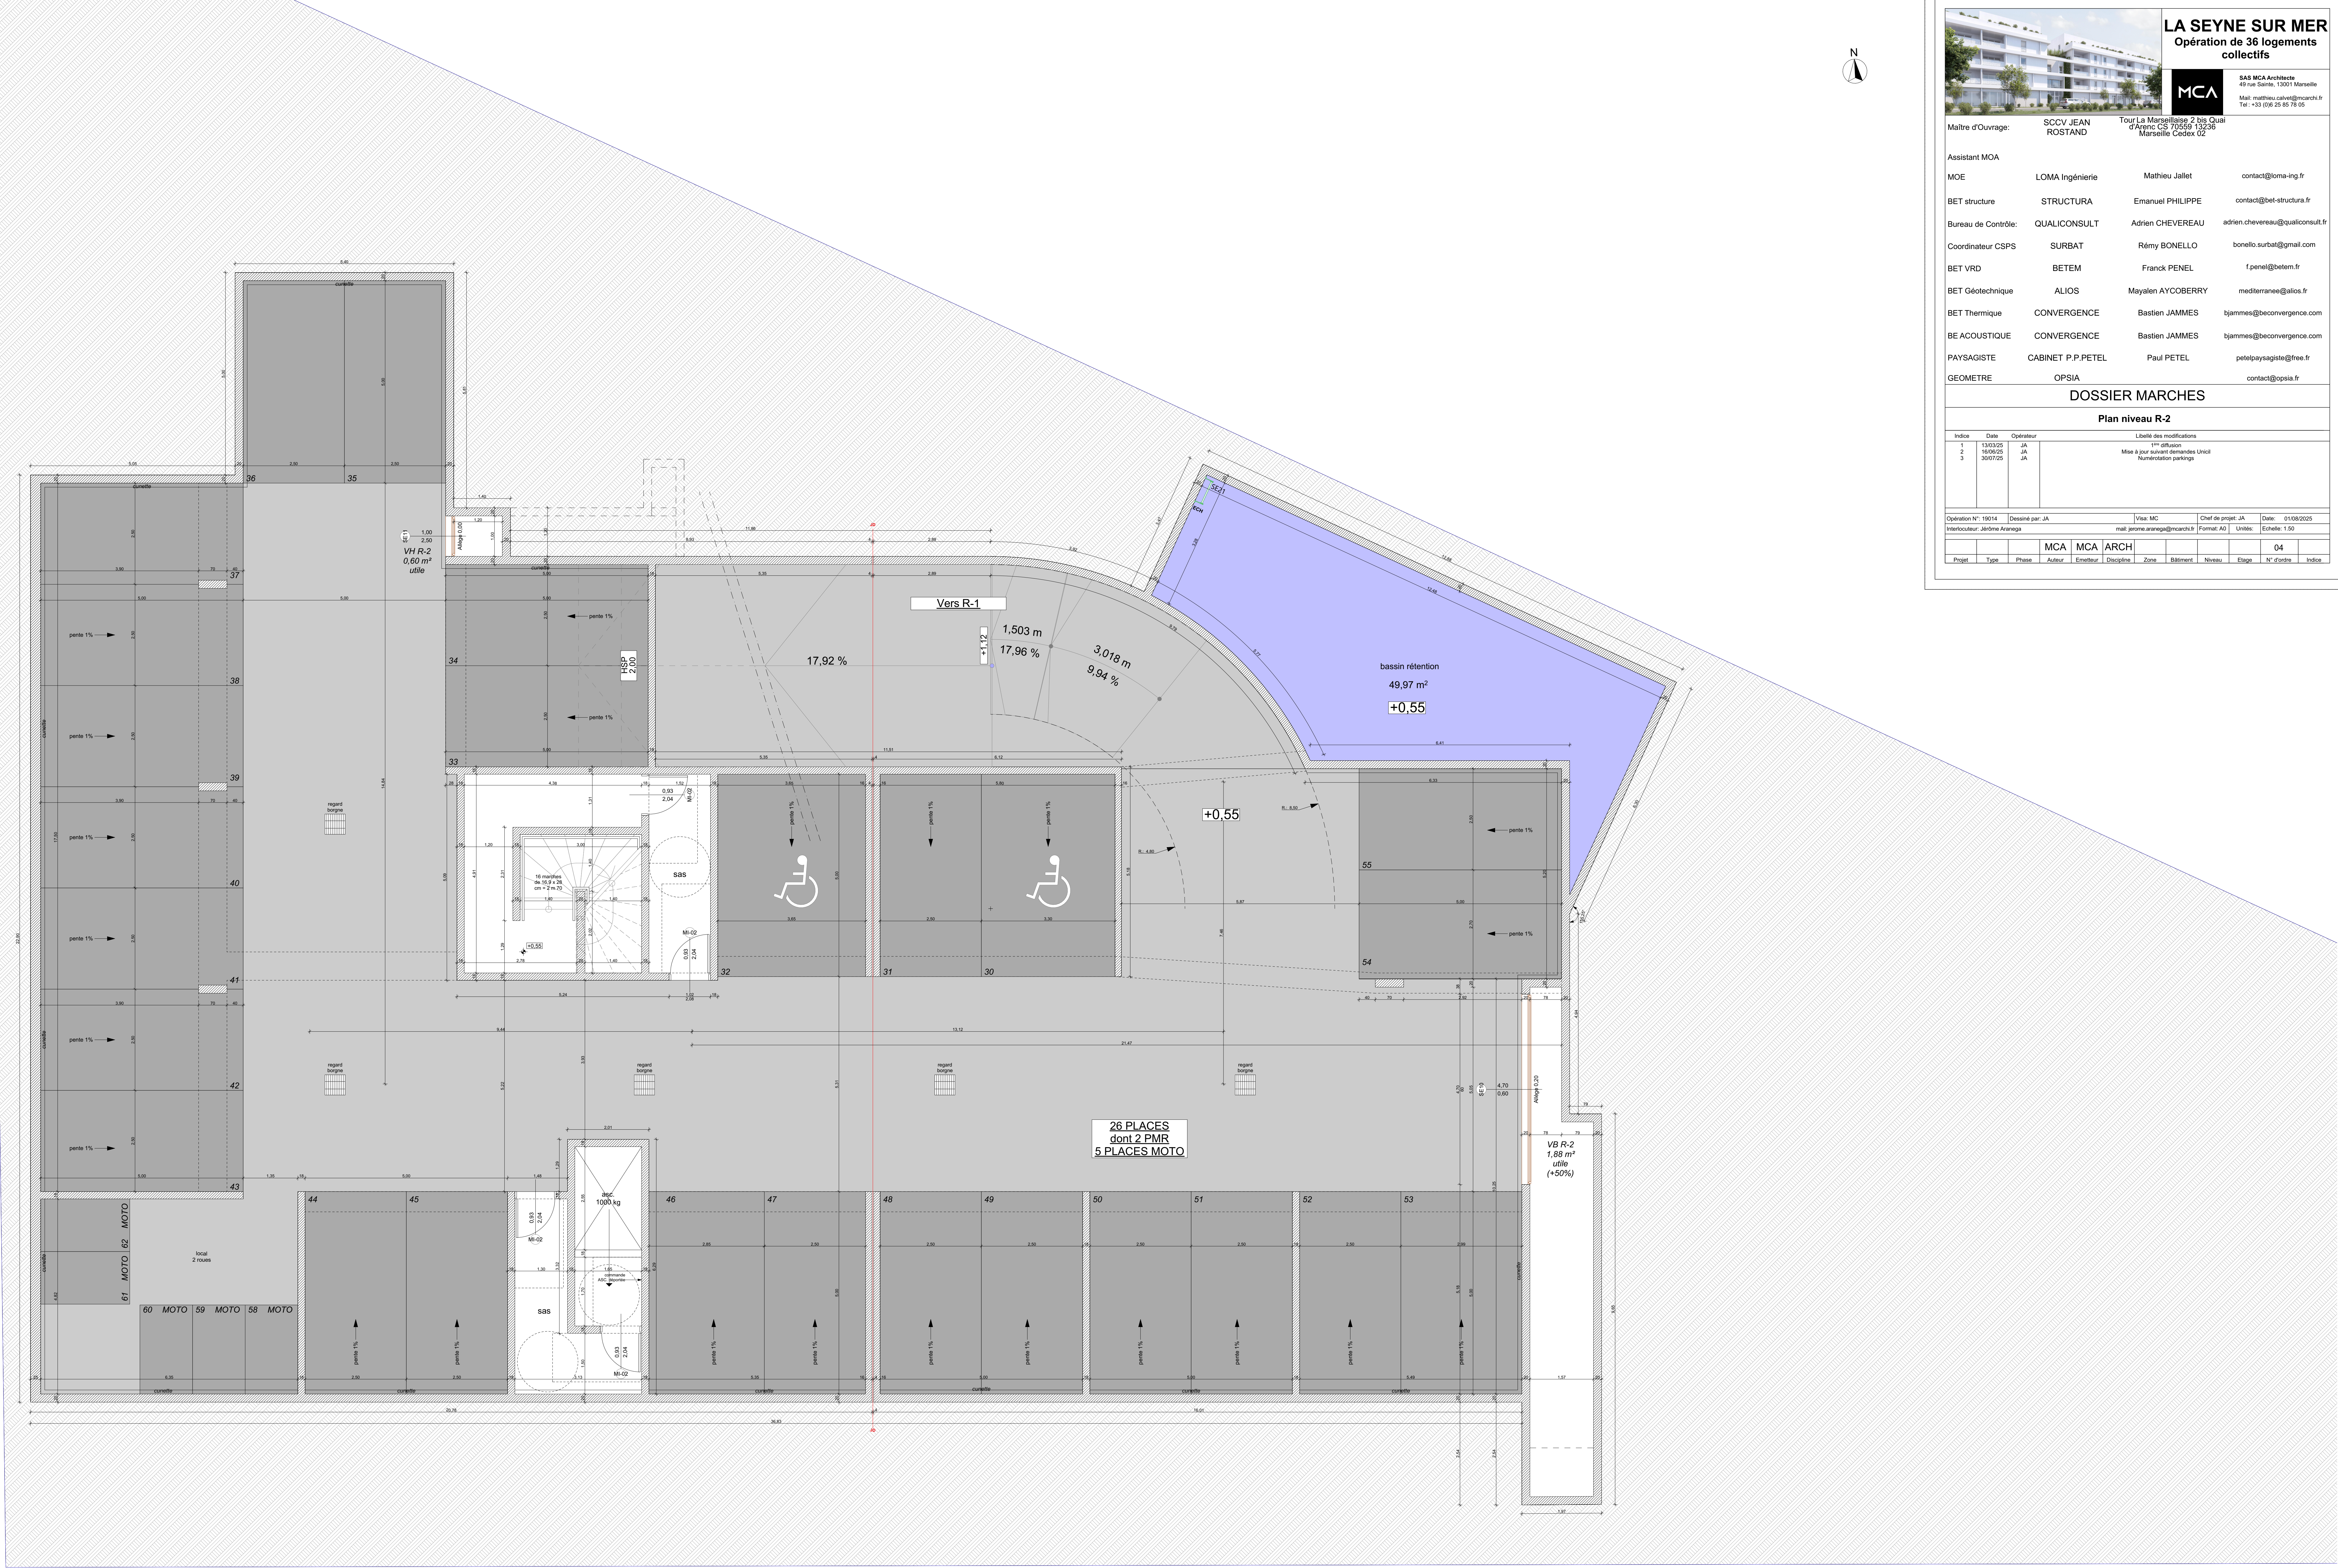

LA SEYNE SUR MER
Opération de 36 logements collectifs

SAS MCA Architects
42 rue Saint- 13001 Marseille
Mail: matthieu.cavelier@mcaarch.fr
Tel: +33 (0)6 25 65 78 05

Maitre d'Ouvrage:	SCCV JEAN ROSTAND	Tour La Marseillaise 2 bis Quai d'Arènes CS 10558 13236 Marseille Cedex 02
Assistant MOA		
MOE	LOMA Ingénierie	Mathieu Jallet contact@loma-ing.fr
BET structure	STRUCTURA	Emanuel PHILIPPE contact@bet-structura.fr
Bureau de Contrôle:	QUALICONSULT	Adrien CHEVEREAU adrien.chevereau@qualiconsult.fr
Coordinateur CSPS	SURBAT	Rémy BONELLO bonello.surbat@gmail.com
BET VRD	BETEM	Franck PENEL f.penel@betem.fr
BET Géotechnique	ALIOS	Mayalen AYOGBERRY mediterrane@alios.fr
BET Thermique	CONVERGENCE	Bastien JAMMES bjammes@beconvergence.com
BE ACOUSTIQUE	CONVERGENCE	Bastien JAMMES bjammes@beconvergence.com
PAYSAGISTE	CABINET P.P.PETEL	Paul PETEL petelpaysagiste@free.fr
GEOMETRE	OPSIA	contact@opsia.fr

DOSSIER MARCHES

Plan niveau R-2

Indice	Date	Opérateur	Libellé des modifications
1	13/03/25	JA	1 ^{ère} diffusion
2	18/06/25	JA	Mise à jour suivant demandes Uncl
3	30/07/25	JA	Numérotation parkings

Opération N°: 19014		Dessiné par: JA			Visé: MC		Chef de projet: JA		Date: 01/08/2025		
Interlocuteur: Jérôme Arange					mail: jerome.arange@mcaarch.fr		Format: A3		Unités: Echelle: 1:50		
				MCA		MCA		ARCH		04	
Projet	Type	Phase	Auteur	Emetteur	Discipline	Zone	Bâtiment	Niveau	Etage	N° d'ordre	Indice