


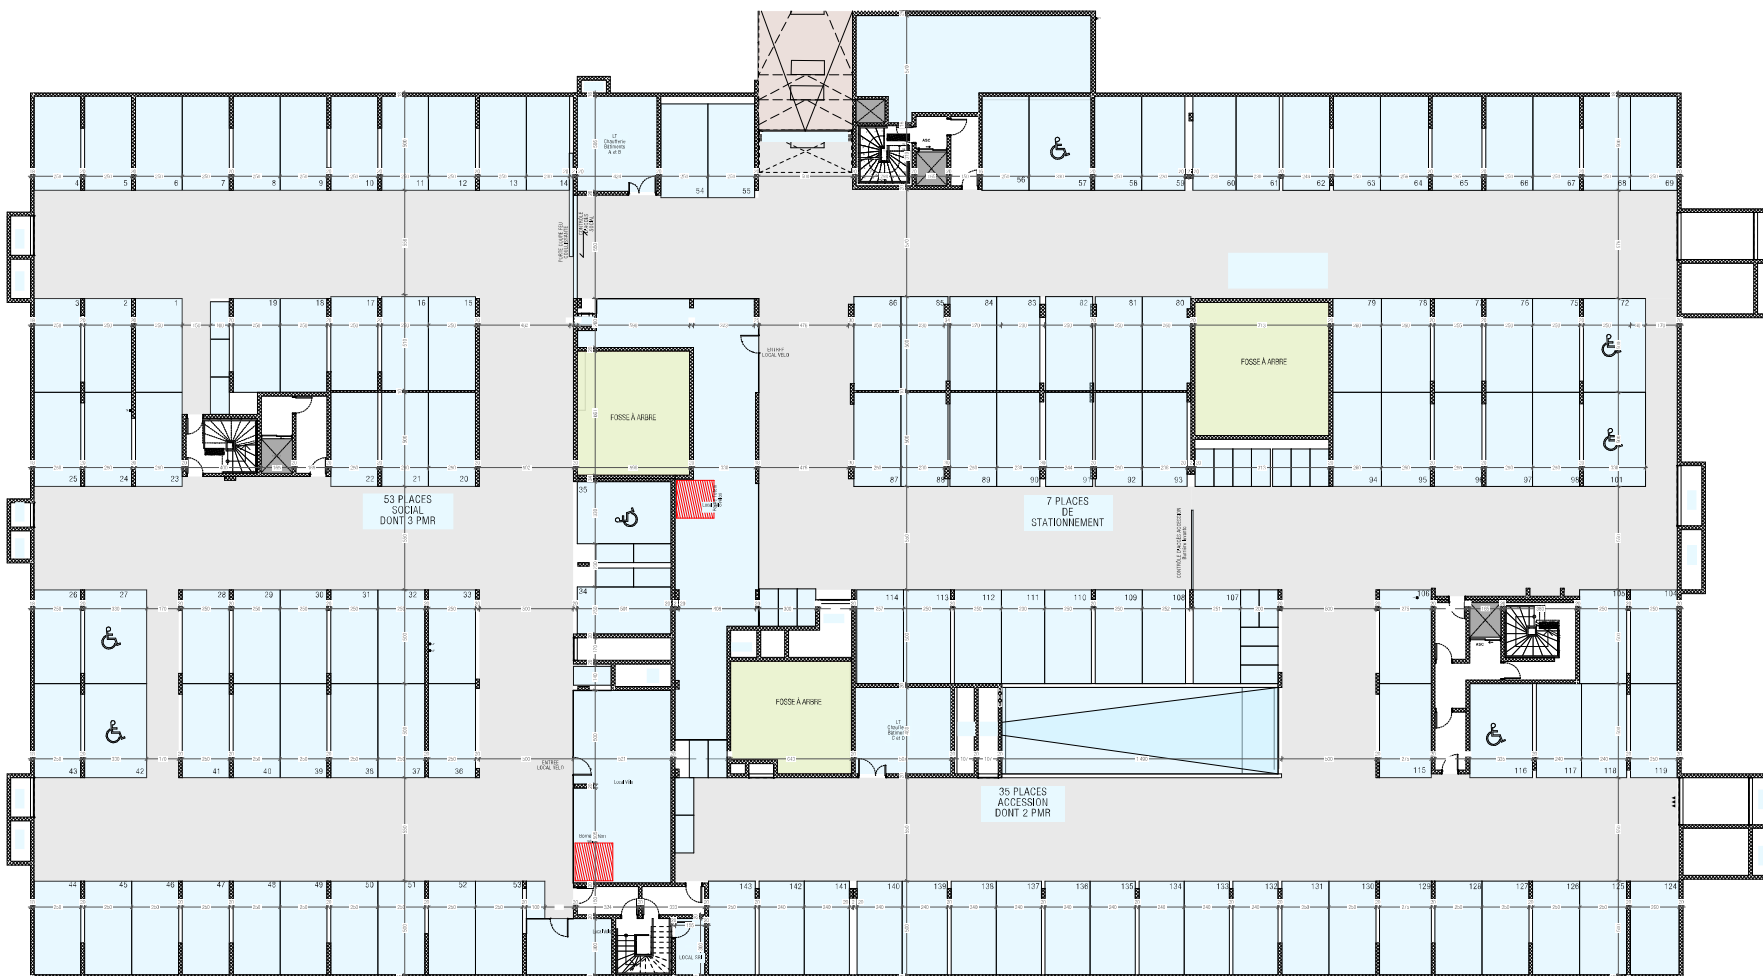

PARC DES ARTS				
343 Boulevard Romain Rolland 13009 MARSEILLE				
PLANS ARCHITECTE				
PROJET DE CONSTRUCTION - ADRESSE: MARSEILLE				
PLANS SYNOPTIQUE				
	01101	SS-2		
	12/06/2023	DCE	Echelle : 1/100	
MAITRE D'OUVRAGE	SNC IMR 65 bis avenue du Prado CS11101 - 13006 Marseille CEDEX			
MAITRE D'OEUVRE	ARCHITECTES SINGULIERS	ARCHITECTES SINGULIERS 14 RUE JEAN JACQUES ROUSSEAU 75001 PARIS ADMINISTRATION@ARCHITECTES-SINGULIERS.COM		
BET STRUCTURE/ FLUIDE/THERMIQUE	BET YVES GARNIER			
BET VRD				
BUREAU DE CONTRÔLE	ALPES CONTROLES			
				



PARC DES ARTS			
343 Boulevard Romain Rolland 13009 MARSEILLE			
PLANS ARCHITECTE			
PROJET DE CONSTRUCTION - PROJET DE REALISATION			
01102		SS-1	
12/06/2023		OCE Echelle : 1/100	
MAITRE D'OUVRAGE	SNC IMR 65 bis avenue de Prado CS11101 - 13006 Marseille CEDEX		
MAITRE D'OEUVRE	ARCHITECTES SINGULIERS		
BET STRUCTURE/ FLUIDE/THERMIQUE	BET YVES GARNIER		
BET VRD			
BUREAU DE CONTROLE	 ALPES CONTROLES		
			